


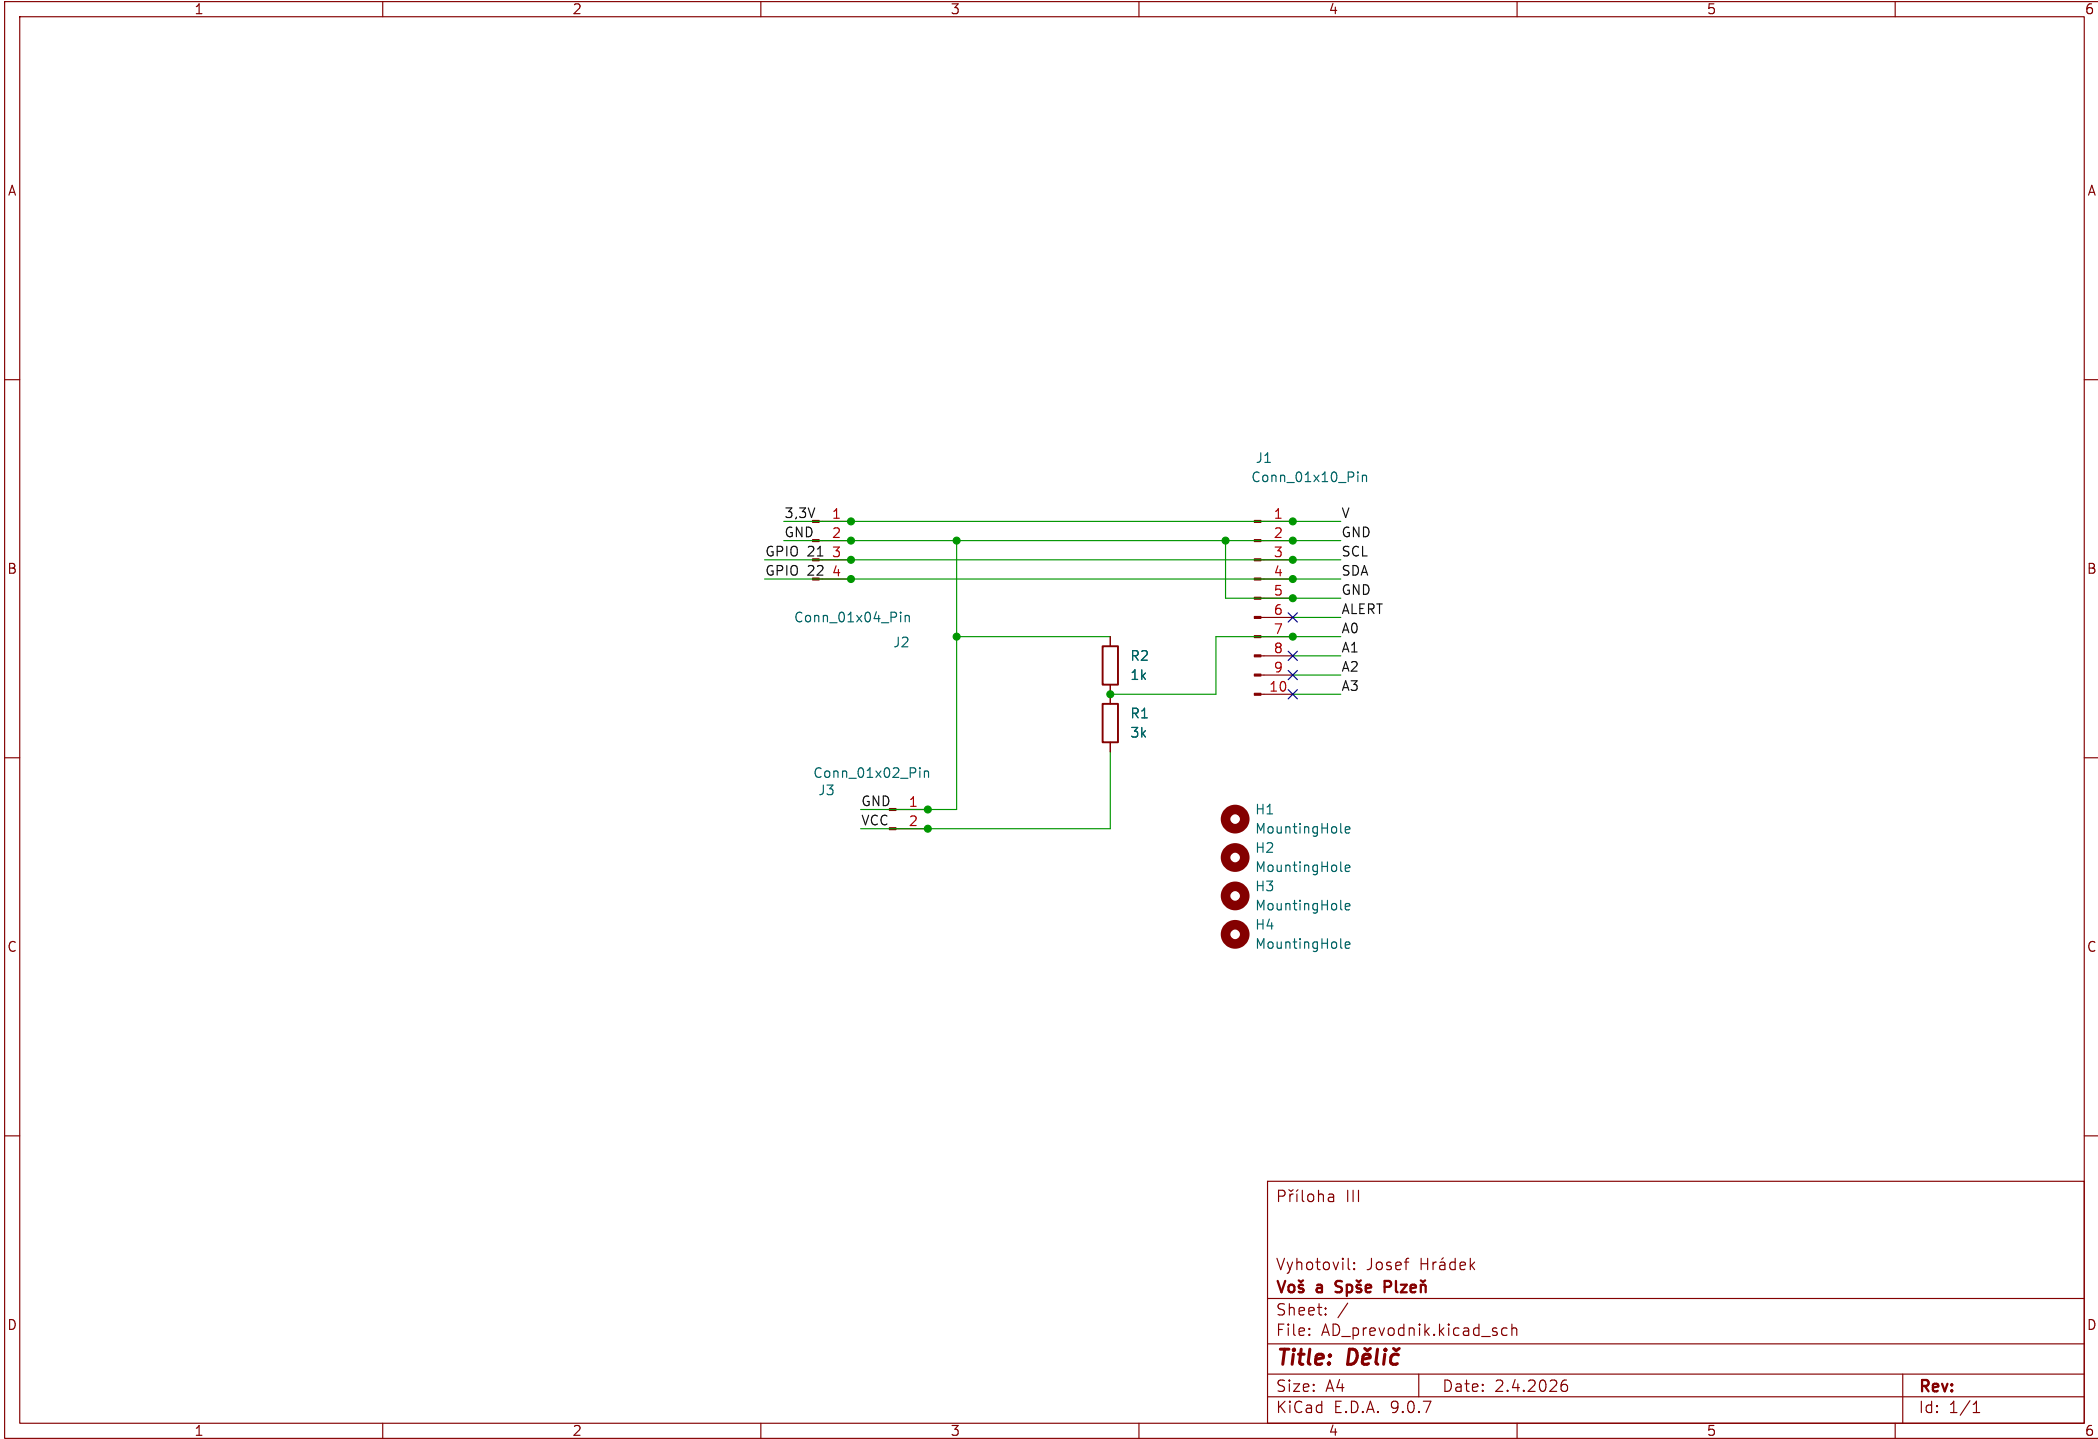

Příloha III		
Vyhotovil: Josef Hrádek		
Voš a Spše Plzeň		
Sheet: /		
File: AD_prevodnik.kicad_sch		
Title: Dělič		
Size: A4	Date: 2.4.2026	Rev:
KiCad E.D.A. 9.0.7	Id: 1/1	